

VALERIE TATE  
&  
GREGORY ARMS  
RESIDENCE


1 Cottage Street  
Belfast, ME 04915  
Waldo County

Architect  
Miche Booz Architect Inc.  
208 Market Street  
Brookville, MD 20833  
301-774-6911  
emvsnrper@michebooz.com

Set Title:  
DRAFT PERMIT SET  
10/01/2021

Revisions:

Key:

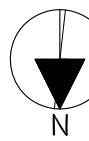


Scale: 1/4" = 1'-0"  
0 1 2 3 4  
INCH  
AT 100%

File:

Drawing Title:  
FIRST FLOOR PLAN

Sheet:  
A-101

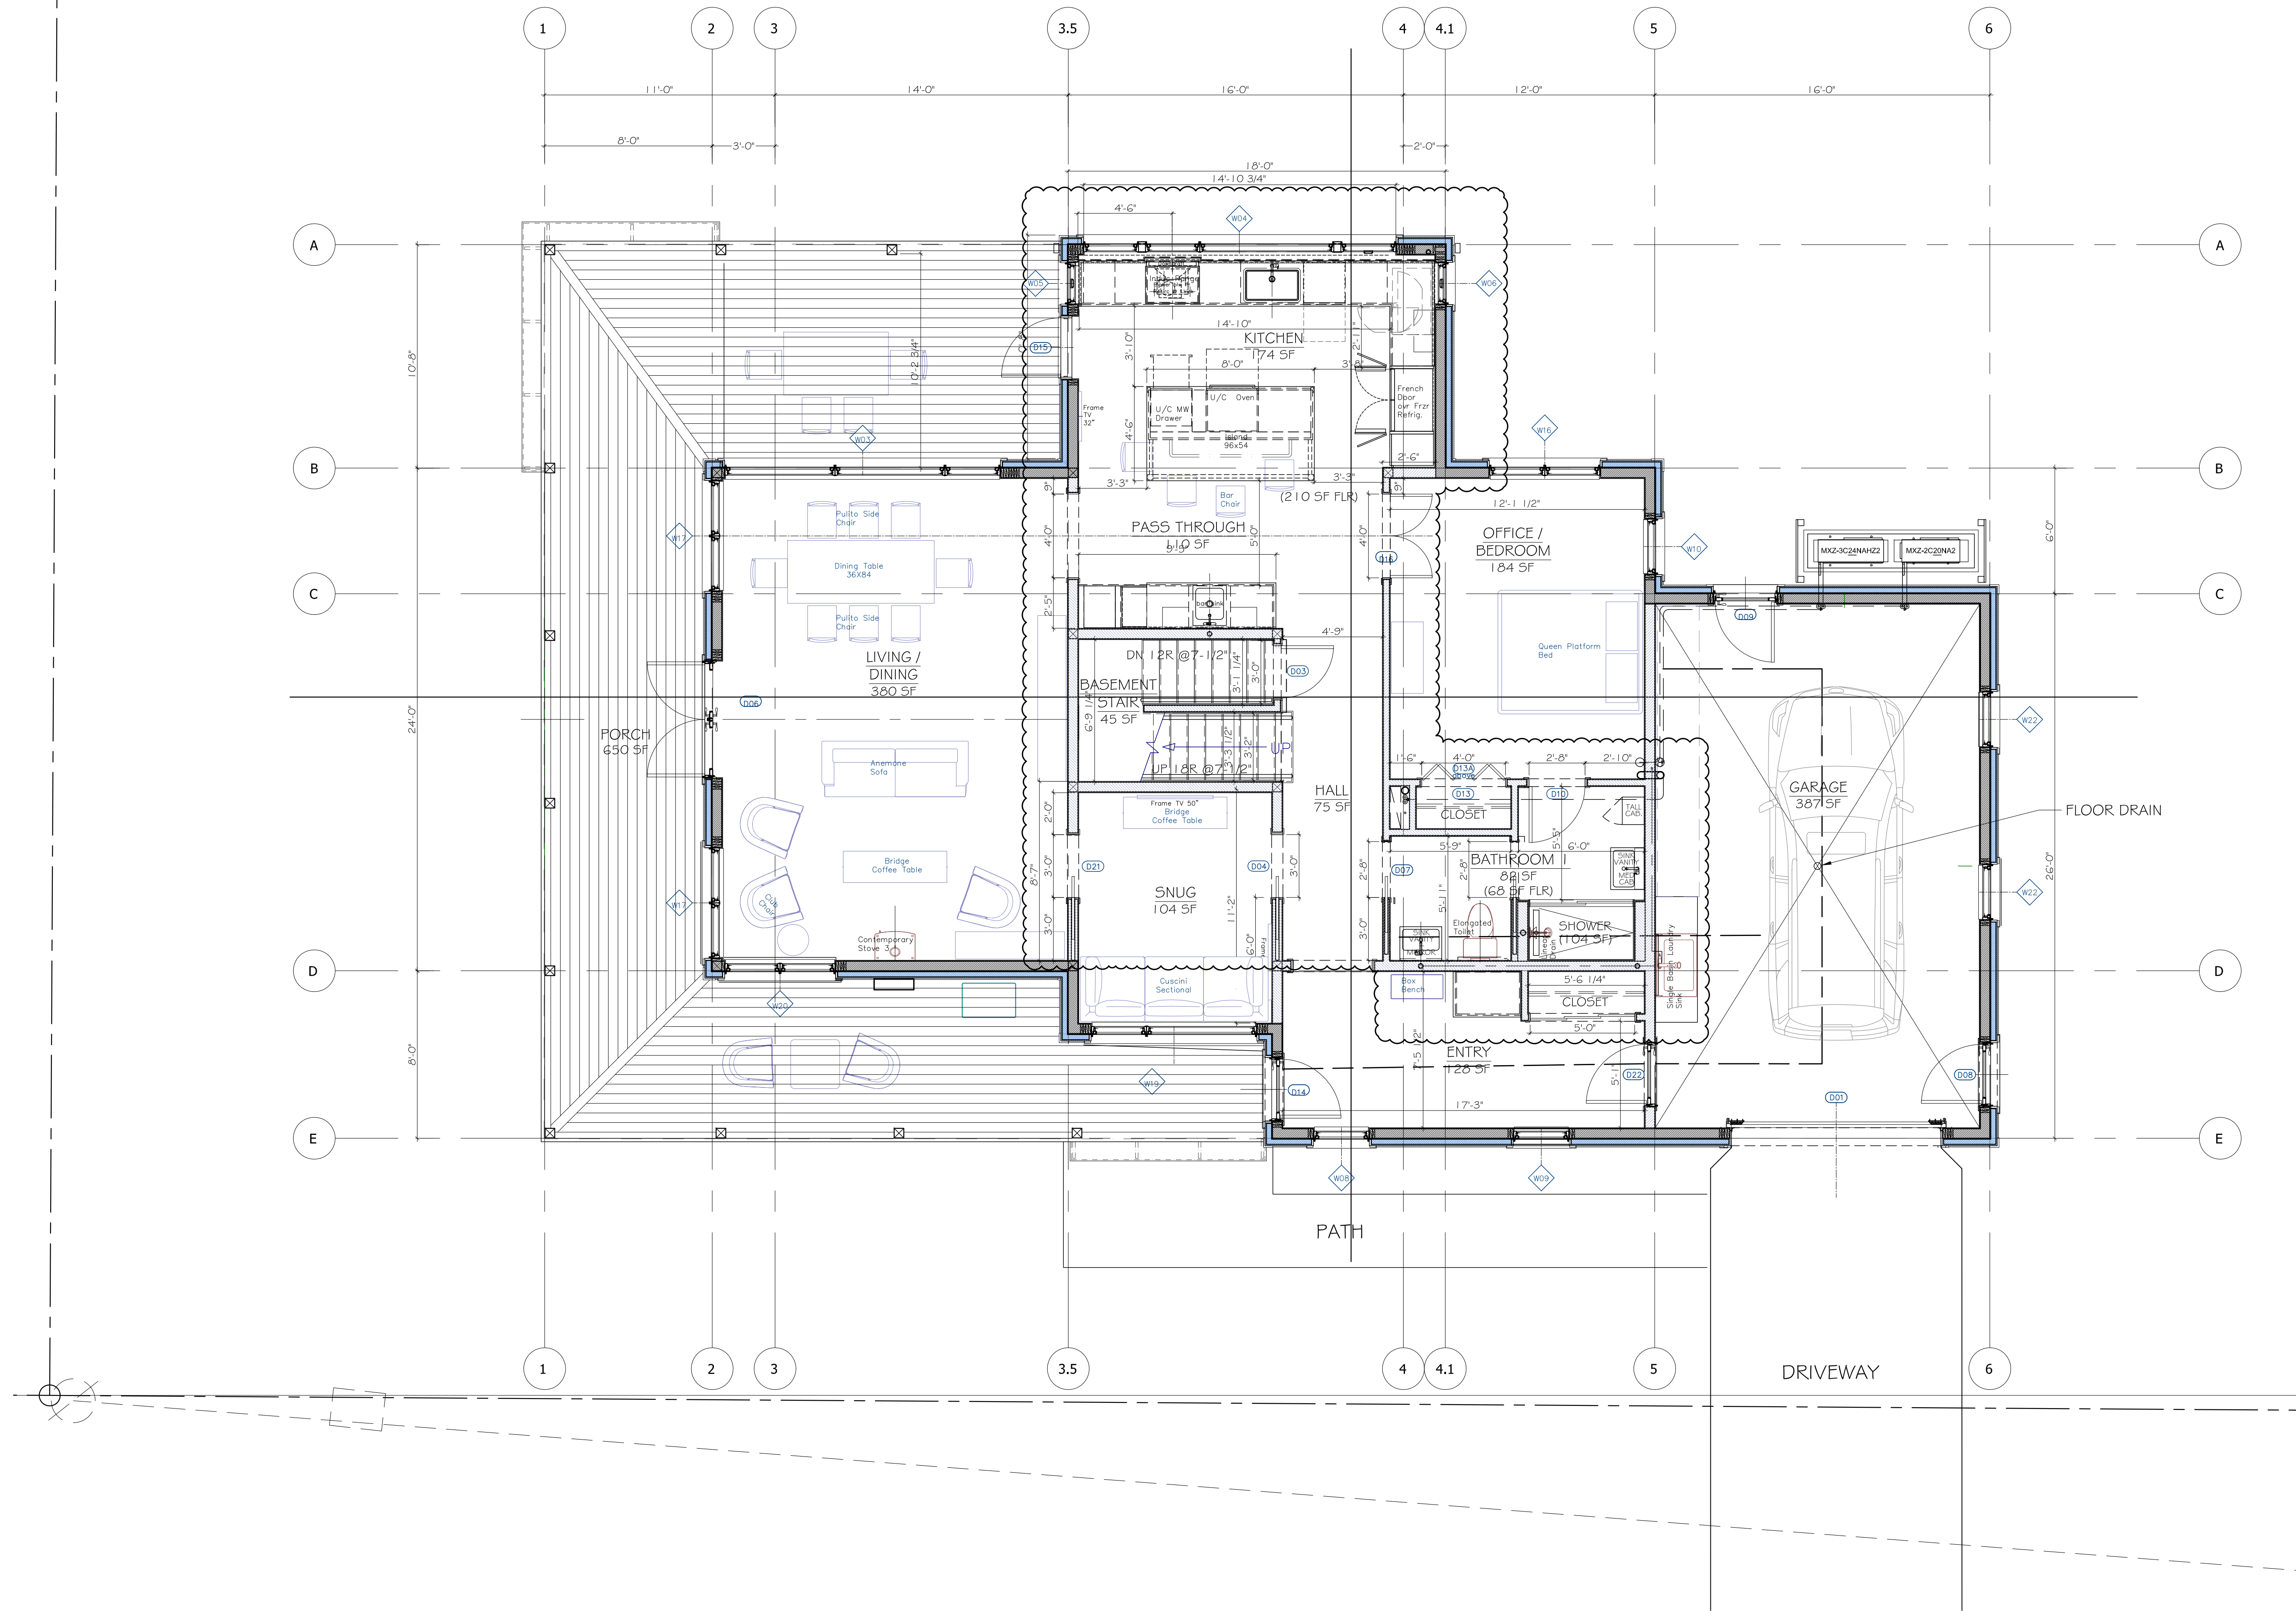

1 PROPOSED FLOOR PLAN