

MICHE BOOZ

ARCHITECT

208 Market St
Brookeville
Maryland 20833
301 774 6911
office@michebooz.com

VALERIE TATE
&
GREGORY ARMS
RESIDENCE


1 Cottage Street
Belfast, ME 04915
Waldo County

Architect
Miche Booz Architect Inc.
208 Market Street
Brookeville, MD 20833
301-774-6911
emvvanriper@michebooz.com

Set Title:
DRAFT PERMIT SET
10/01/2021

Revisions:

Key:

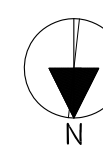


Scale: 1/4" = 1'-0"
0 1 2 3 4
INCH
AT 100%

File:

Drawing Title:
SECOND FLOOR PLAN

Sheet:
A-102

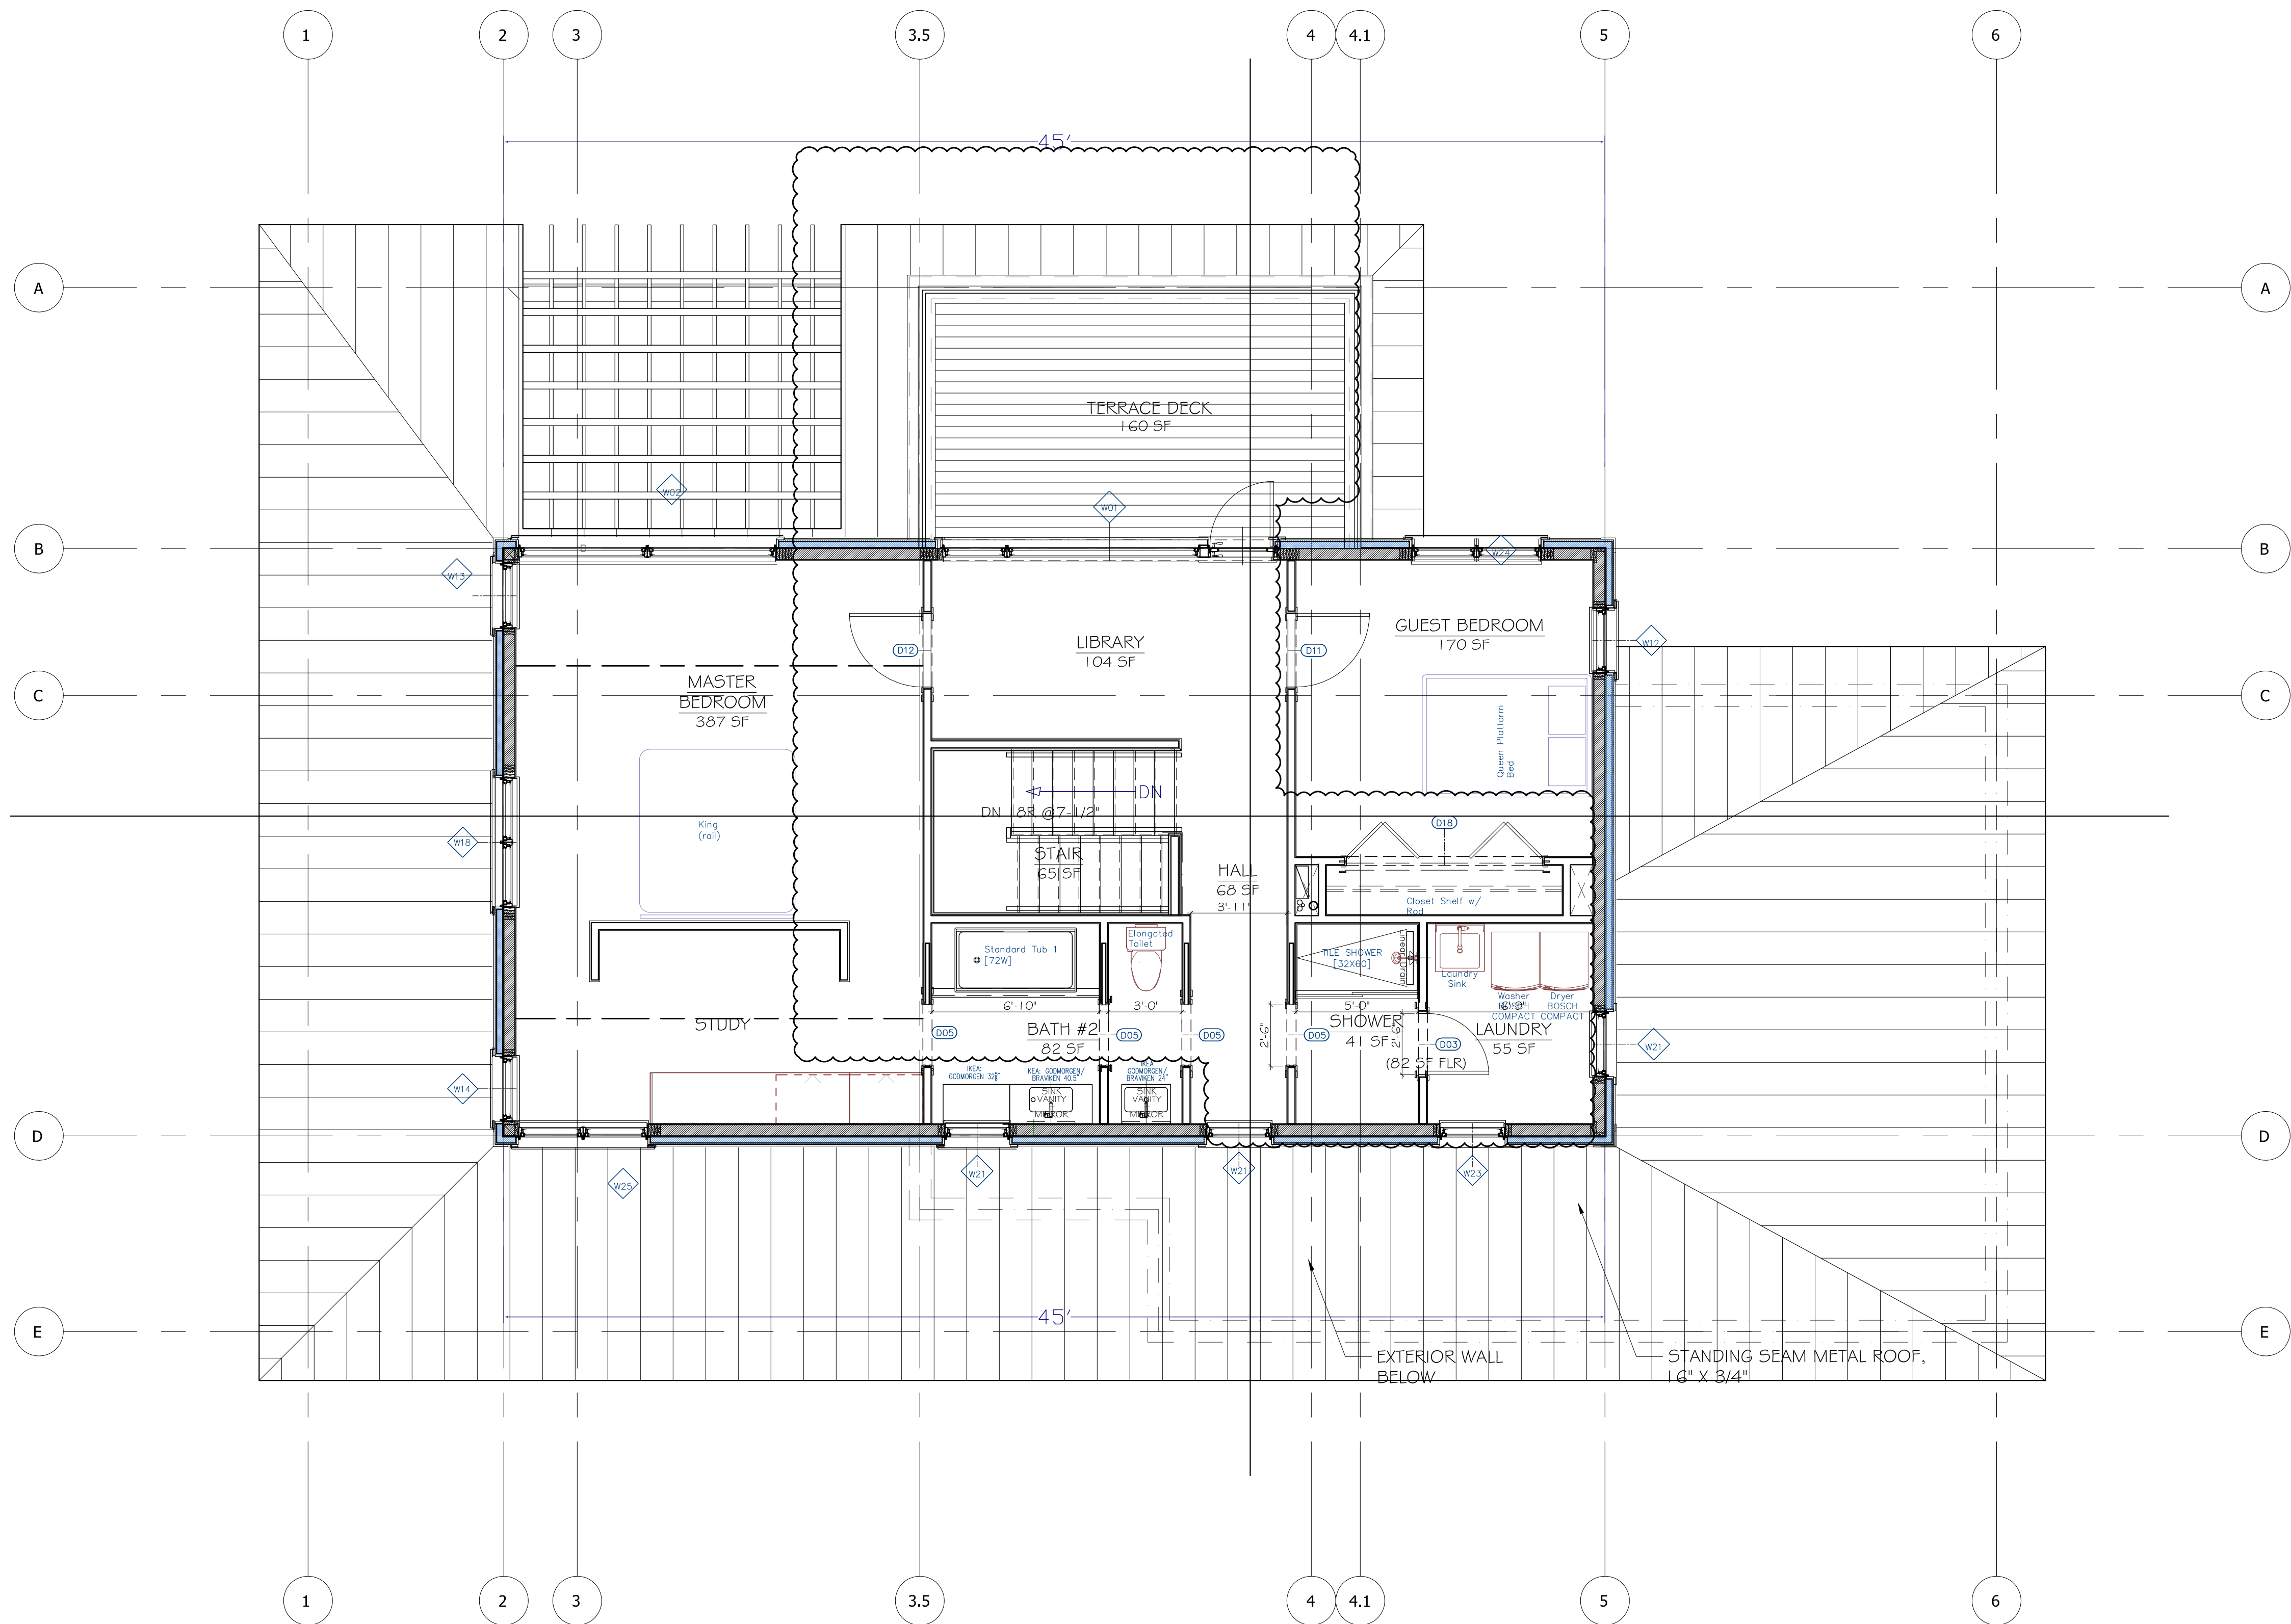

1 PROPOSED FLOOR PLAN